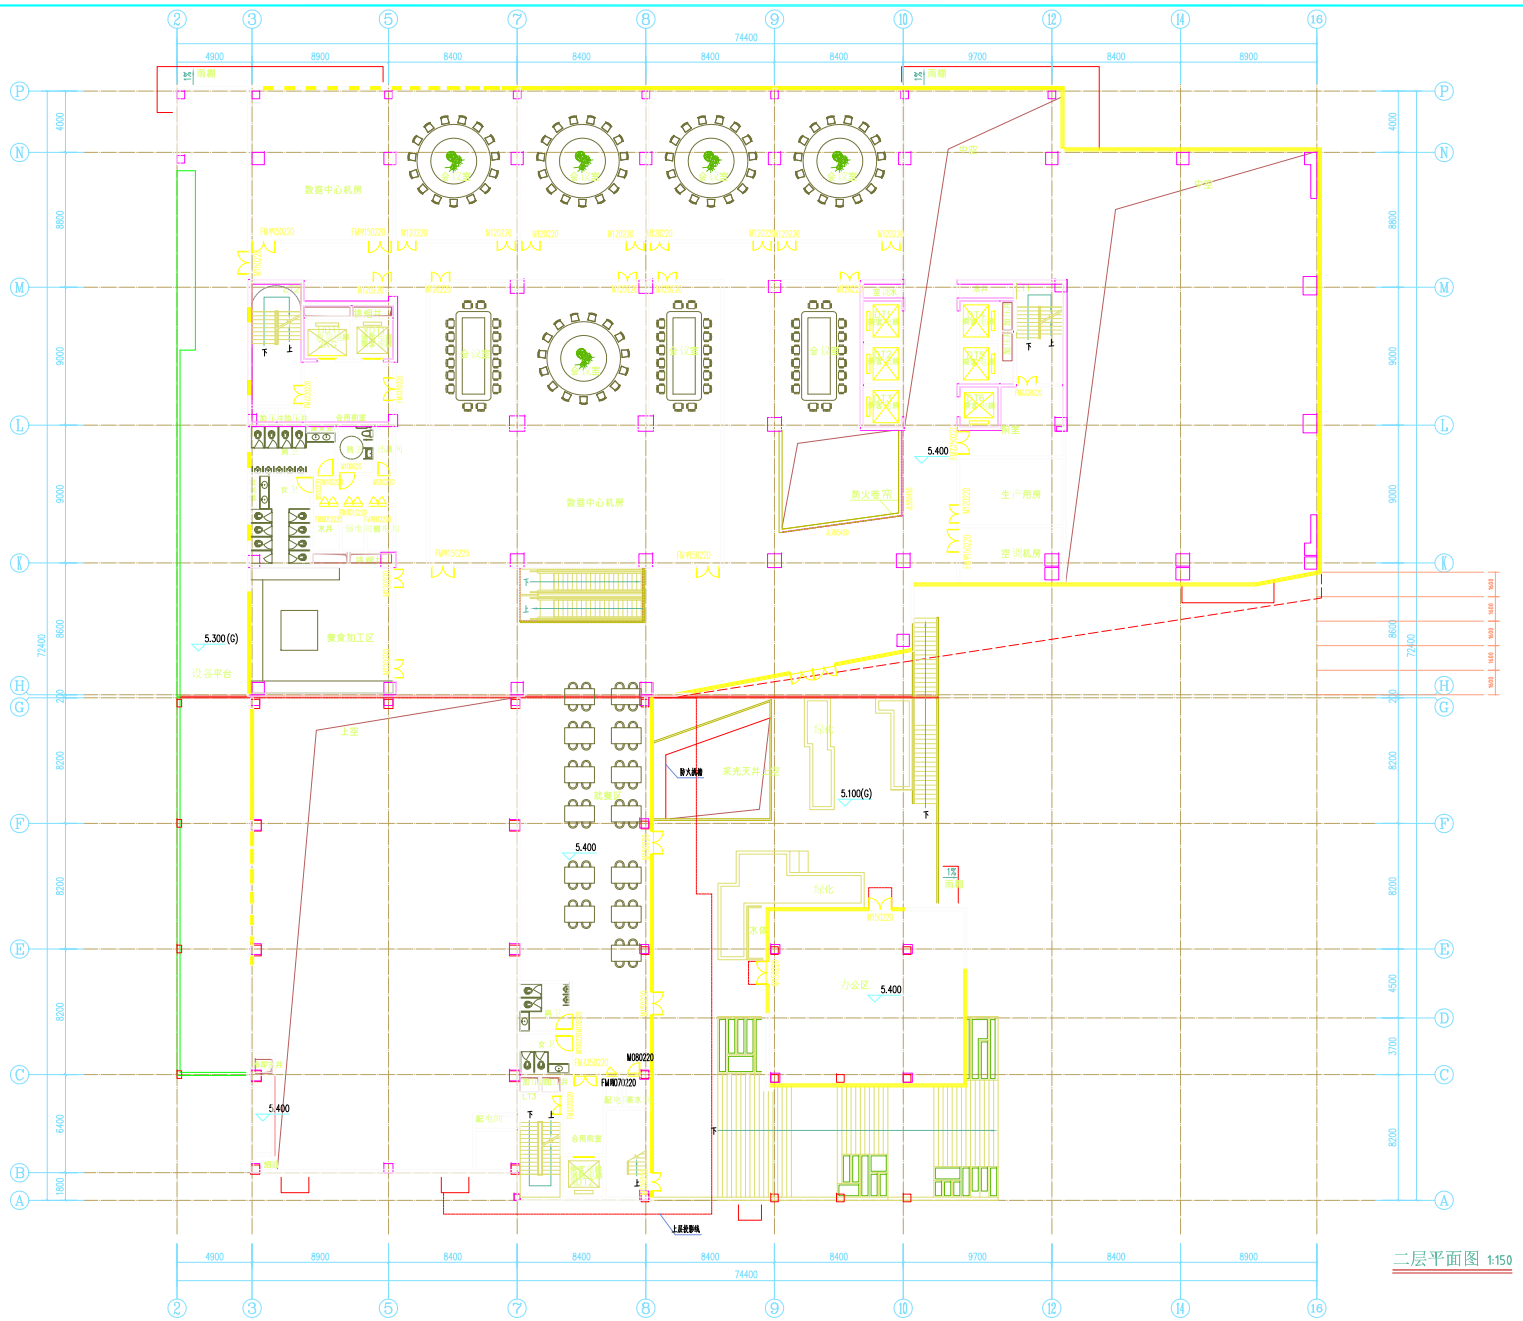

二层平面图 1:150

会签栏	建筑	结构	暖通空调
给排水	电气	装修	弱电系统

JSD 景森設計

项目名称: 广州迈普再生医学科技股份有限公司总部基地项目		
建设单位: 广州迈普再生医学科技股份有限公司		
审定	林少斌	
项目负责	陆伟	
专业负责	谢家峰	
审核	陆伟	
校对	李冠南	
设计	崔琬莹	
制图	崔琬莹	
图名: 二层平面图 JD楼二层平面图		
图纸比例	1:150	阶段 报建
工程编号	JJS-1-1800	专业 建筑
图号	J-01-PM05	日期 2019.06

景森设计股份有限公司
JINGSEN DESIGN CO., LTD.

建筑工程设计甲级：A144014193